


Nomenclatura das peças no CorteCloud
Direita e Esquerda é como referência o módulo
e não quem está de frente para o módulo

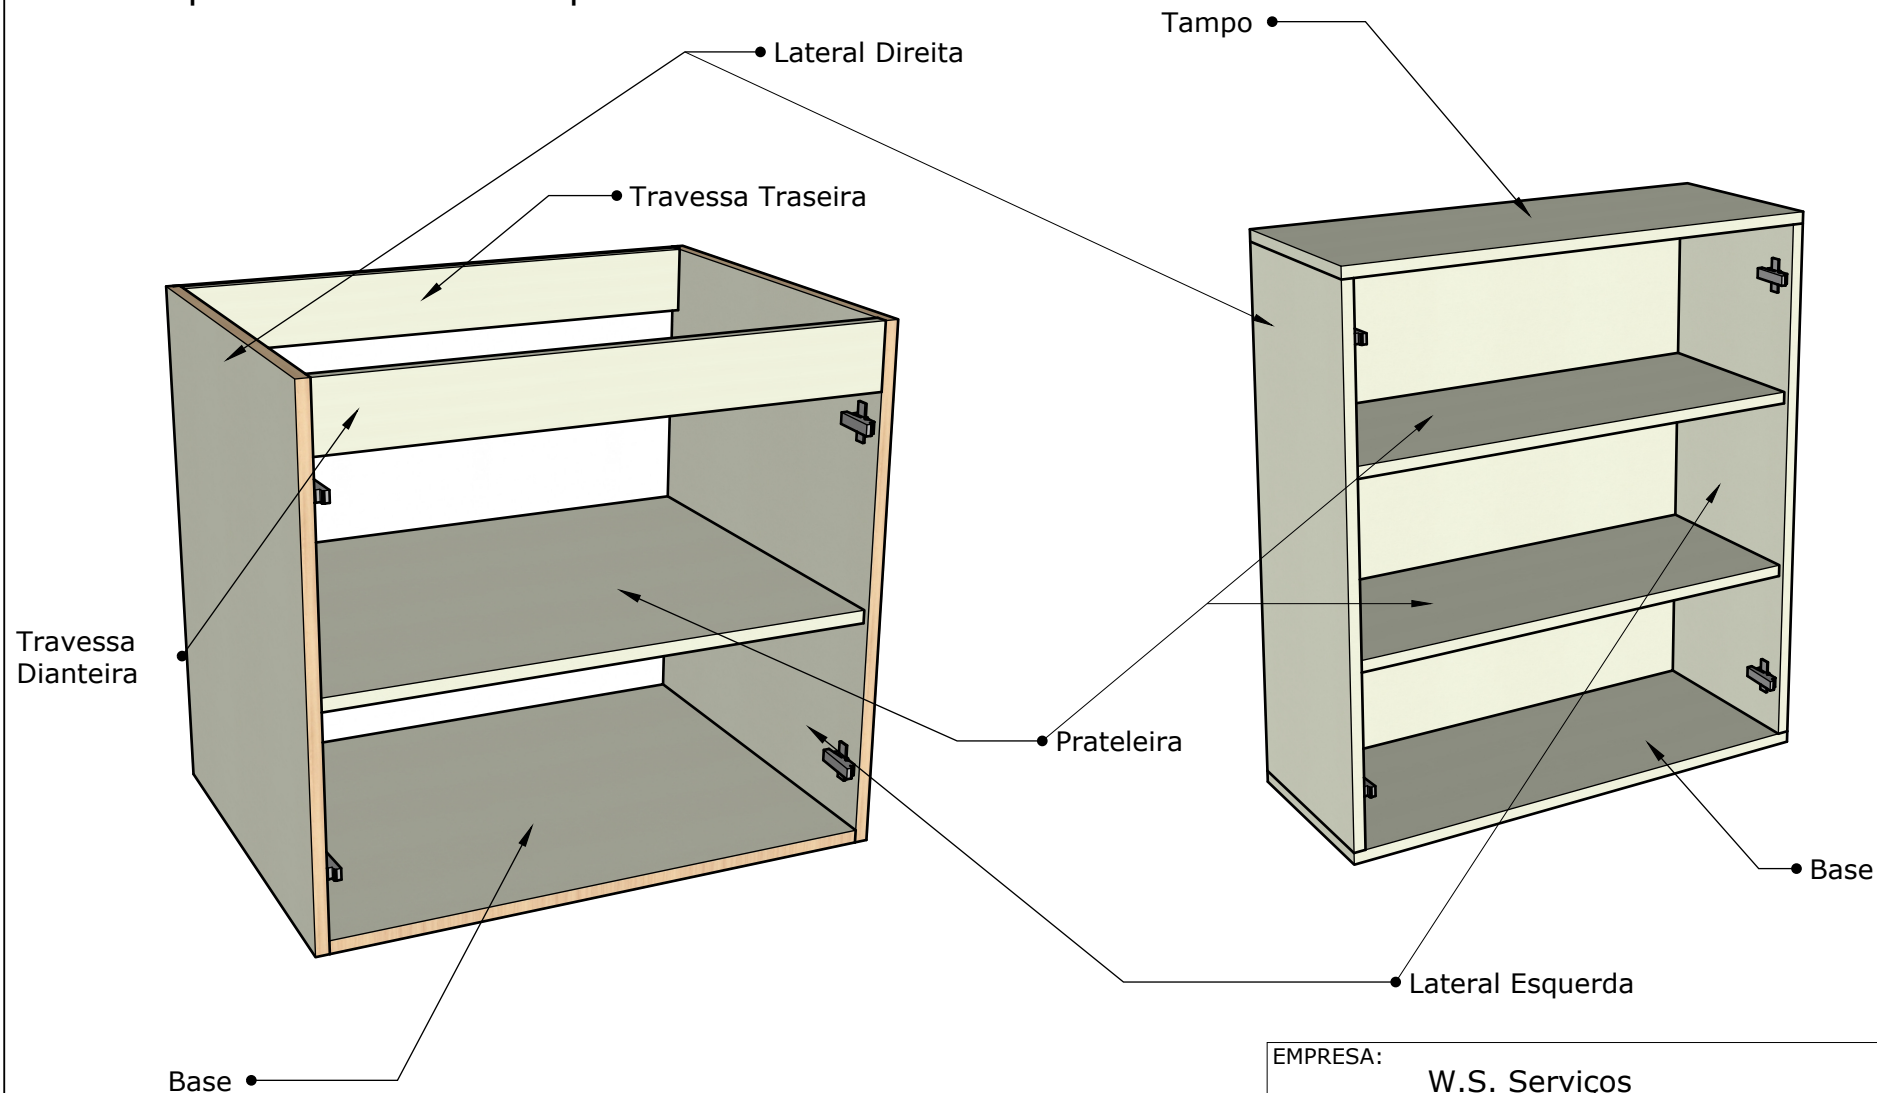

EMPRESA:	W.S. Serviços
PROJETISTA:	Willian Scariott de Souza www.omarceneirodigital.com.br
CLIENTE:	Rodrigo e Bruna

Página: 1

Etiquetas

Padrão do MDF e espessura



• Orientação sobre o módulo ou função da peça

• Nome do módulo no sistema. às vezes um módulo pode ser usado para outra função. Ex: um módulo de "Balcão 1 porta" para ser usado como base para um gaveteiro com gavetas avulsas com medidas personalizadas.


Esse número entre parênteses é único para cada módulo. Todas as peças que tiverem o mesmo número pertencem ao mesmo módulo. Não existe duas peças com mesmo número que não seja do mesmo módulo.

• Função da peça no módulo.
 Ex: Lateral direita ou esquerda, base, tampo, prateleira, travessa dianteira ou traseira, painel, tamponamento, vista, etc.

Toda peça tem uma etiqueta com informações. Peças sem etiqueta são sobras. Pode acontecer de alguma etiqueta se descolar, não descartar as peças sem etiqueta até final da instalação.

EMPRESA:	W.S. Serviços
PROJETISTA:	Willian Scariott de Souza www.omarceneirodigital.com.br
CLIENTE:	Rodrigo e Bruna

Roupeiro

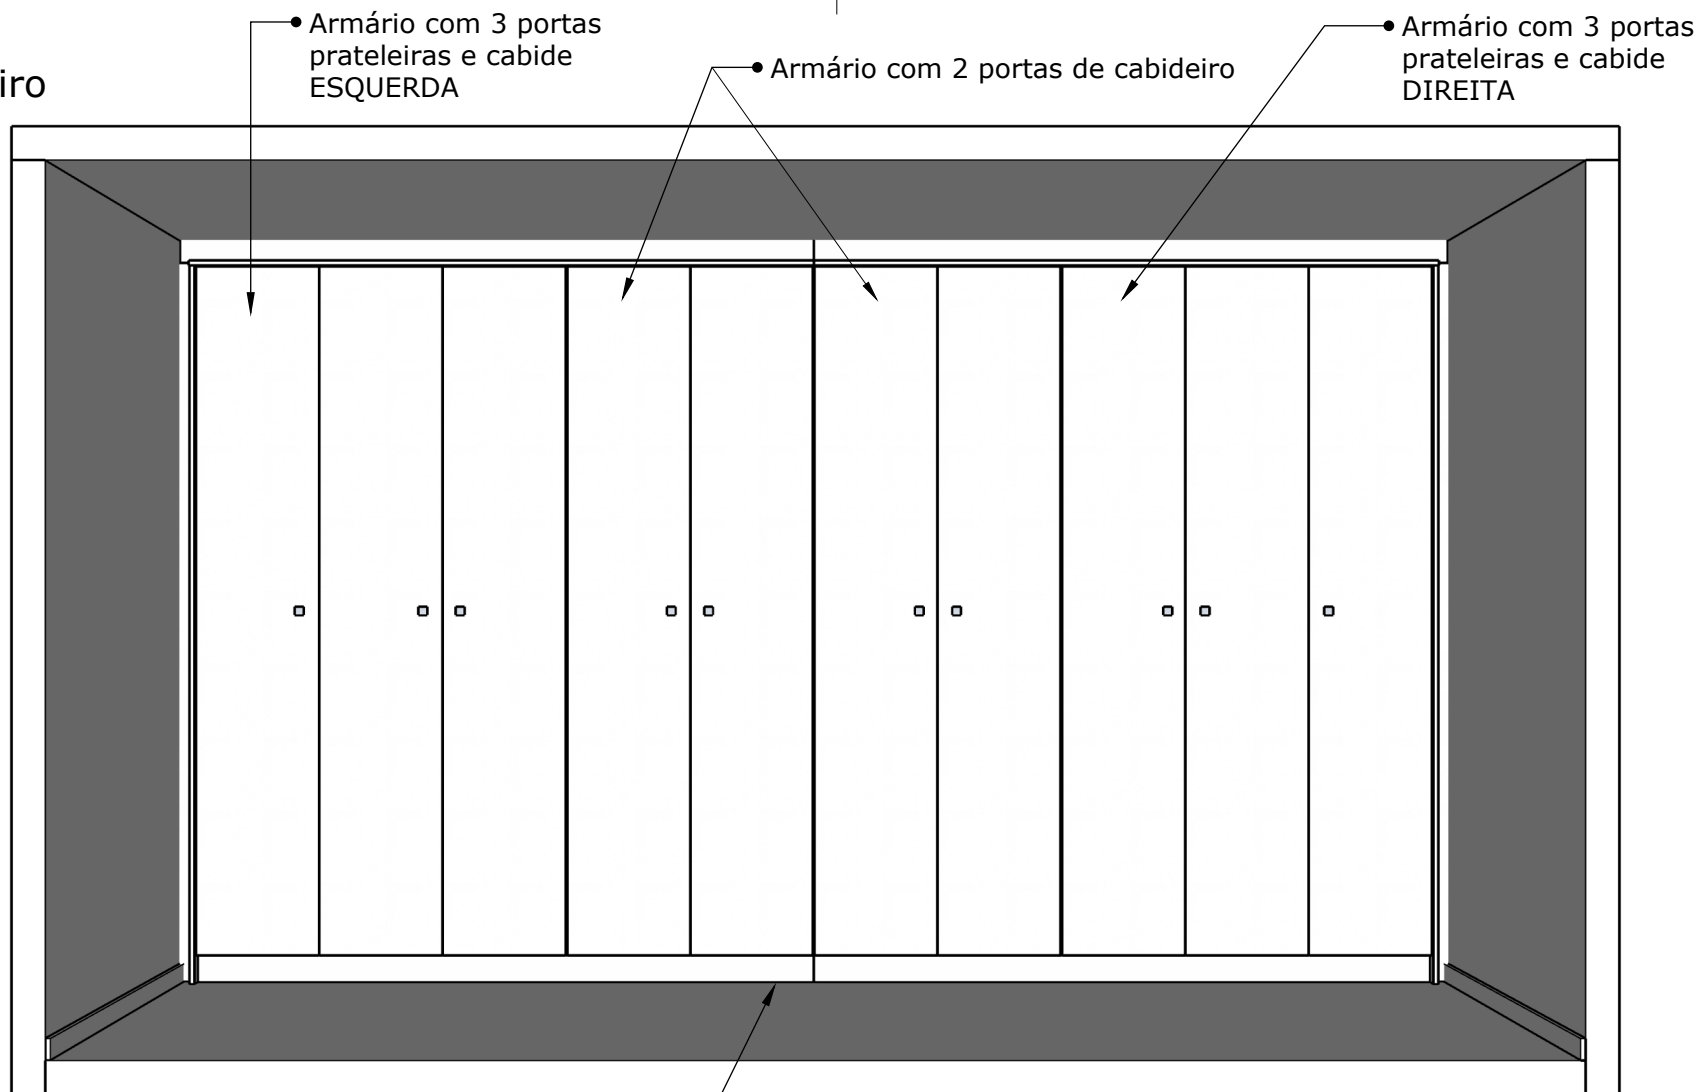

Rodapé em 2 partes
Instalar e nivelar o rodapé
antes de apoiar os armários

EMPRESA:

W.S. Serviços

PROJETISTA:

Willian Scariott de Souza

www.omarceneirodigital.com.br

CLIENTE:

Rodrigo e Bruna

Página: 3

Roupeiro


Vista vertical
para fechamento
cortar de acordo
com vão livre
70 x 2585

• Vista horizontal para fechamento de teto
ajustar à altura conforme necessário
4560 x 100 (em duas partes)

• Vista vertical
para fechamento
cortar de acordo
com vão livre
70 x 2585

• Dobradiças curvas
o resto é dobradiças retas

• Tamponamento avança 22mm

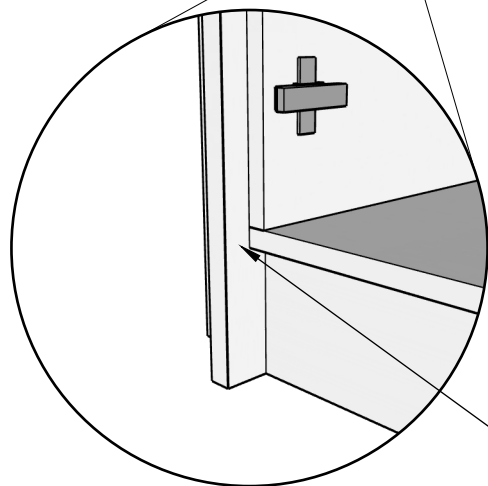

EMPRESA:

W.S. Serviços

PROJETISTA:

Willian Scariott de Souza


www.omarceneirodigital.com.br

CLIENTE:

Rodrigo e Bruna

Página: 4

Roupeiro Rodapé

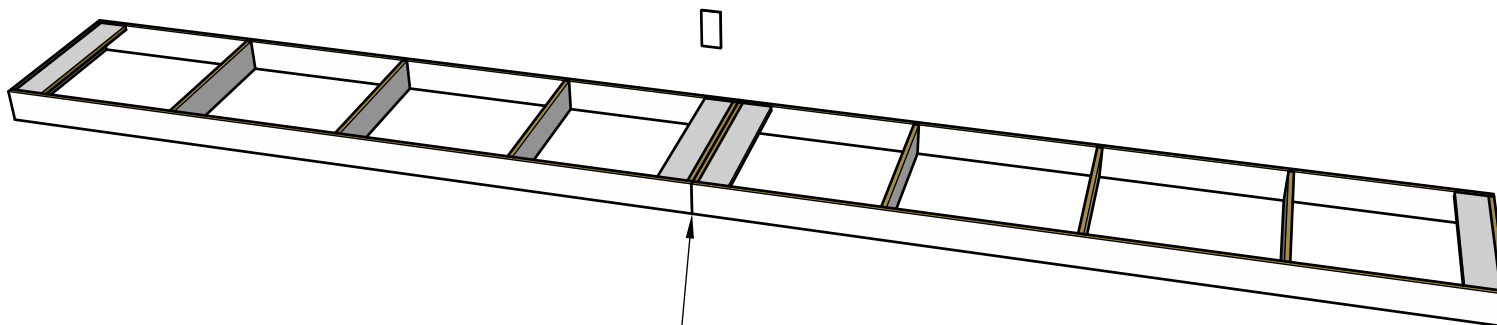


Rodapé em duas partes.
Montador com cantoneira zamak
por dentro para não aparecer
parafusos na frente
Nivelar o rodapé antes de
colocar os armários em
cima.
Pode usar tacos de sobras para nivelar
por dentro do rodapé e parafusar. •

EMPRESA:	W.S. Serviços
PROJETISTA:	Willian Scariott de Souza www.omarceneirodigital.com.br
CLIENTE:	Rodrigo e Bruna

Página: 5

Roupeiro

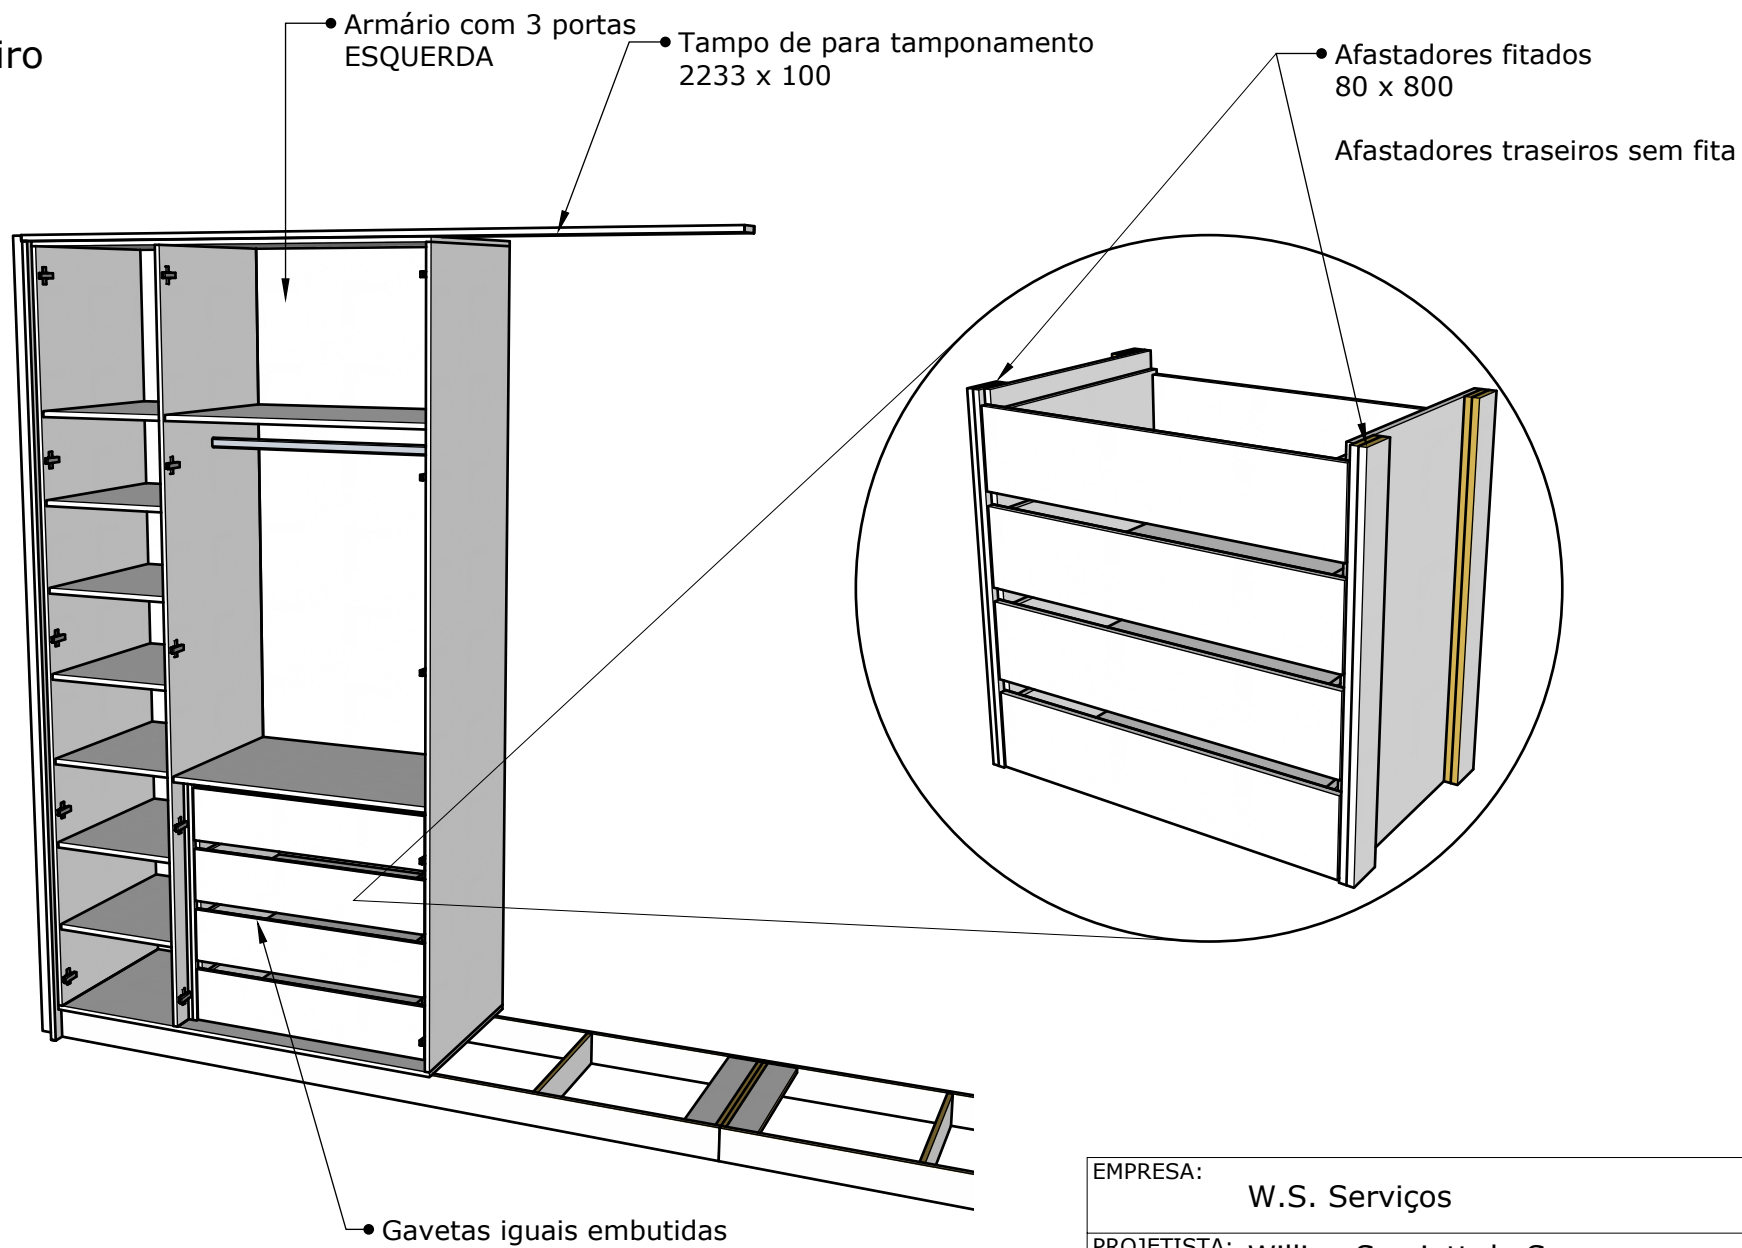

EMPRESA:

W.S. Serviços

PROJETISTA:

Willian Scariott de Souza


www.omarceneirodigital.com.br

CLIENTE:

Rodrigo e Bruna

Página: 6

Roupeiro

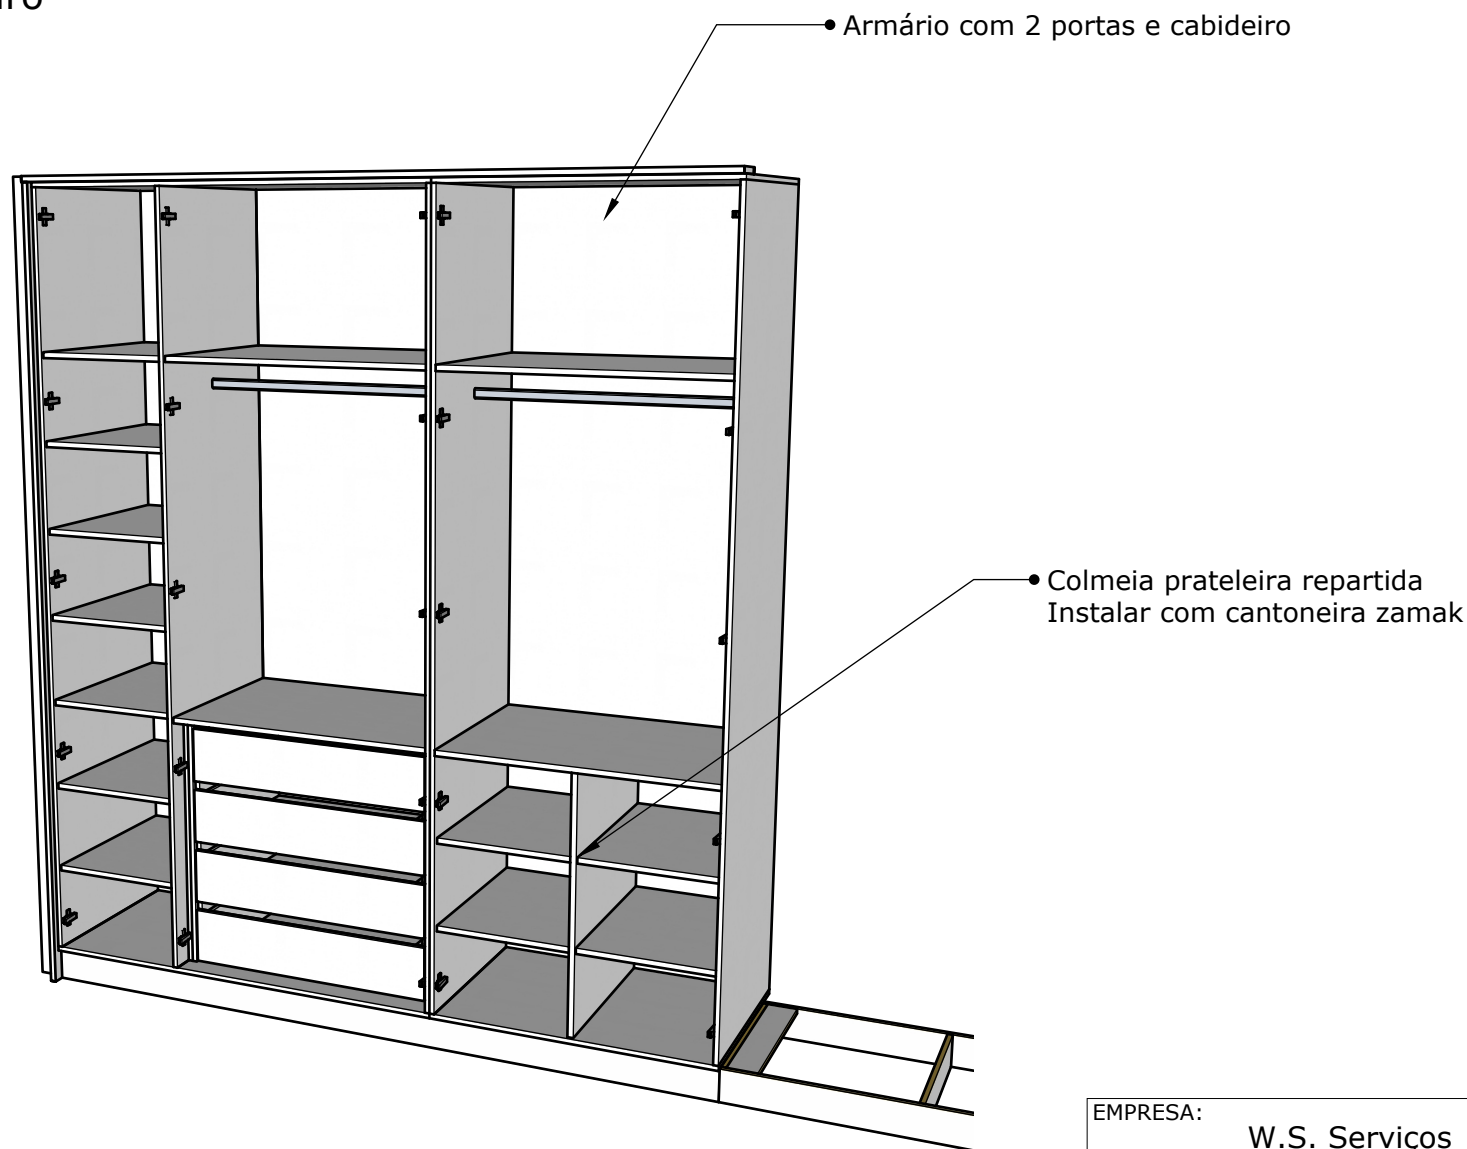

EMPRESA:

W.S. Serviços

PROJETISTA:

Willian Scariott de Souza


www.omarceneirodigital.com.br

CLIENTE:

Rodrigo e Bruna

Página: 7

Roupeiro

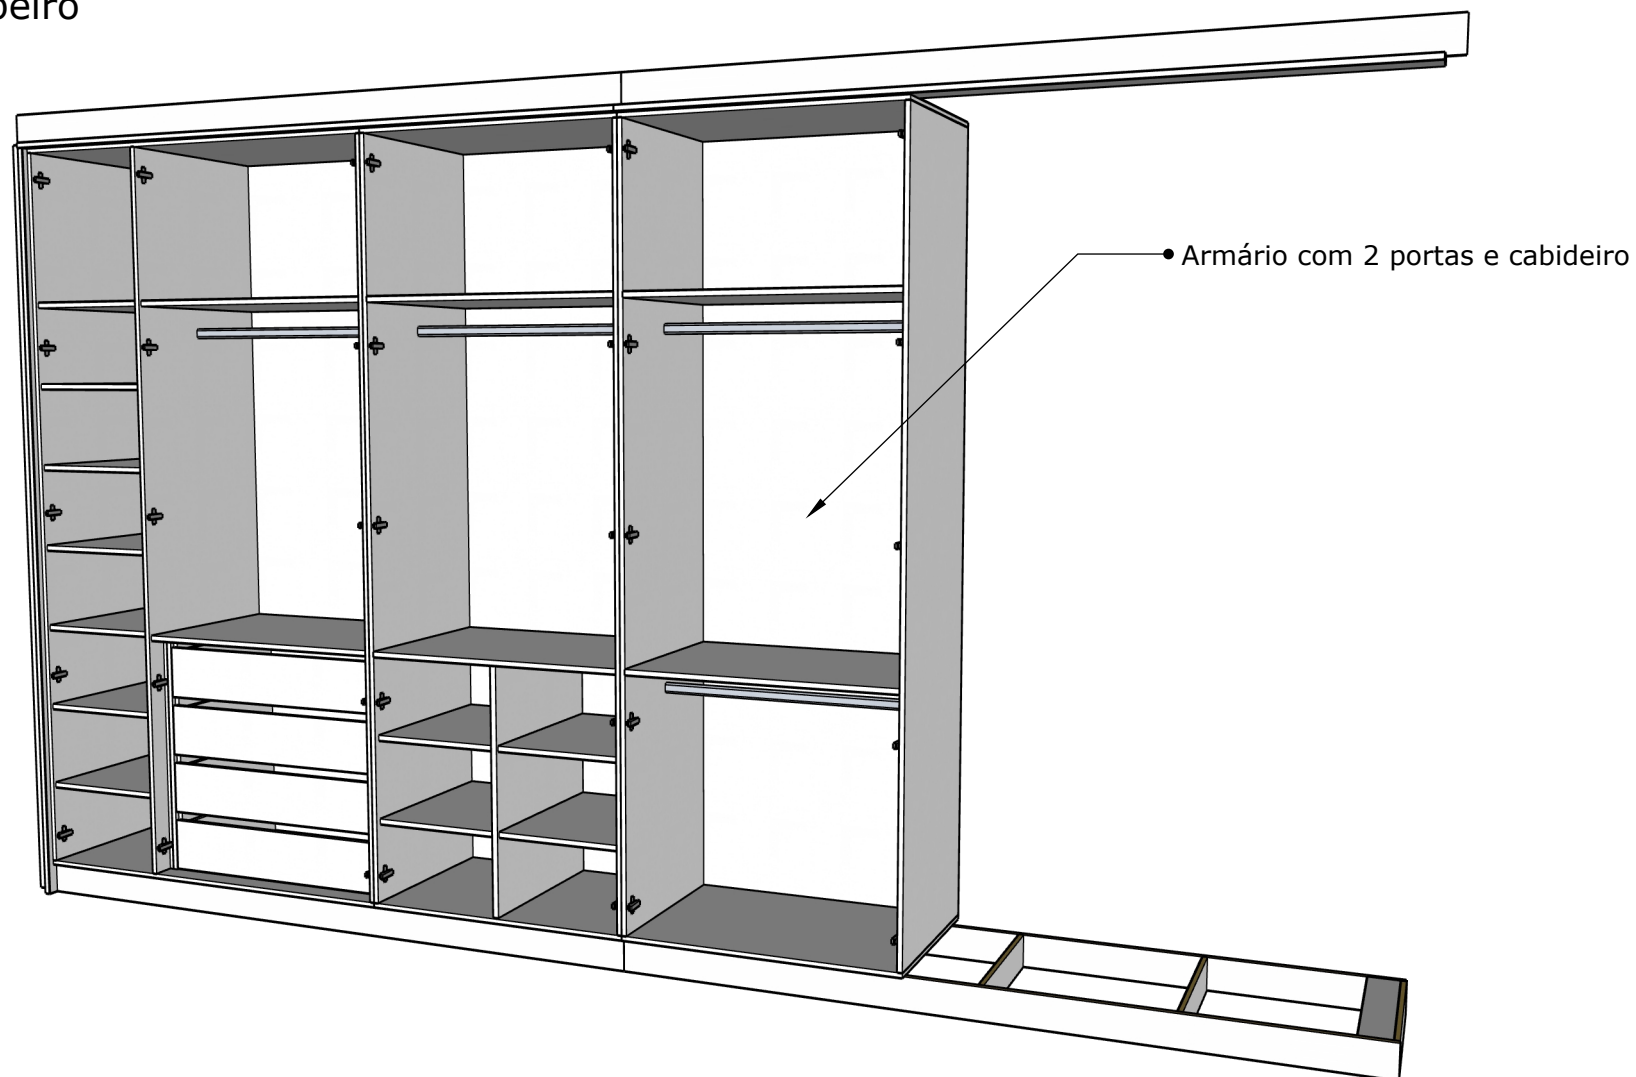

EMPRESA:

W.S. Serviços

PROJETISTA:

Willian Scariott de Souza


www.omarceneirodigital.com.br

CLIENTE:

Rodrigo e Bruna

Página: 8

Roupeiro

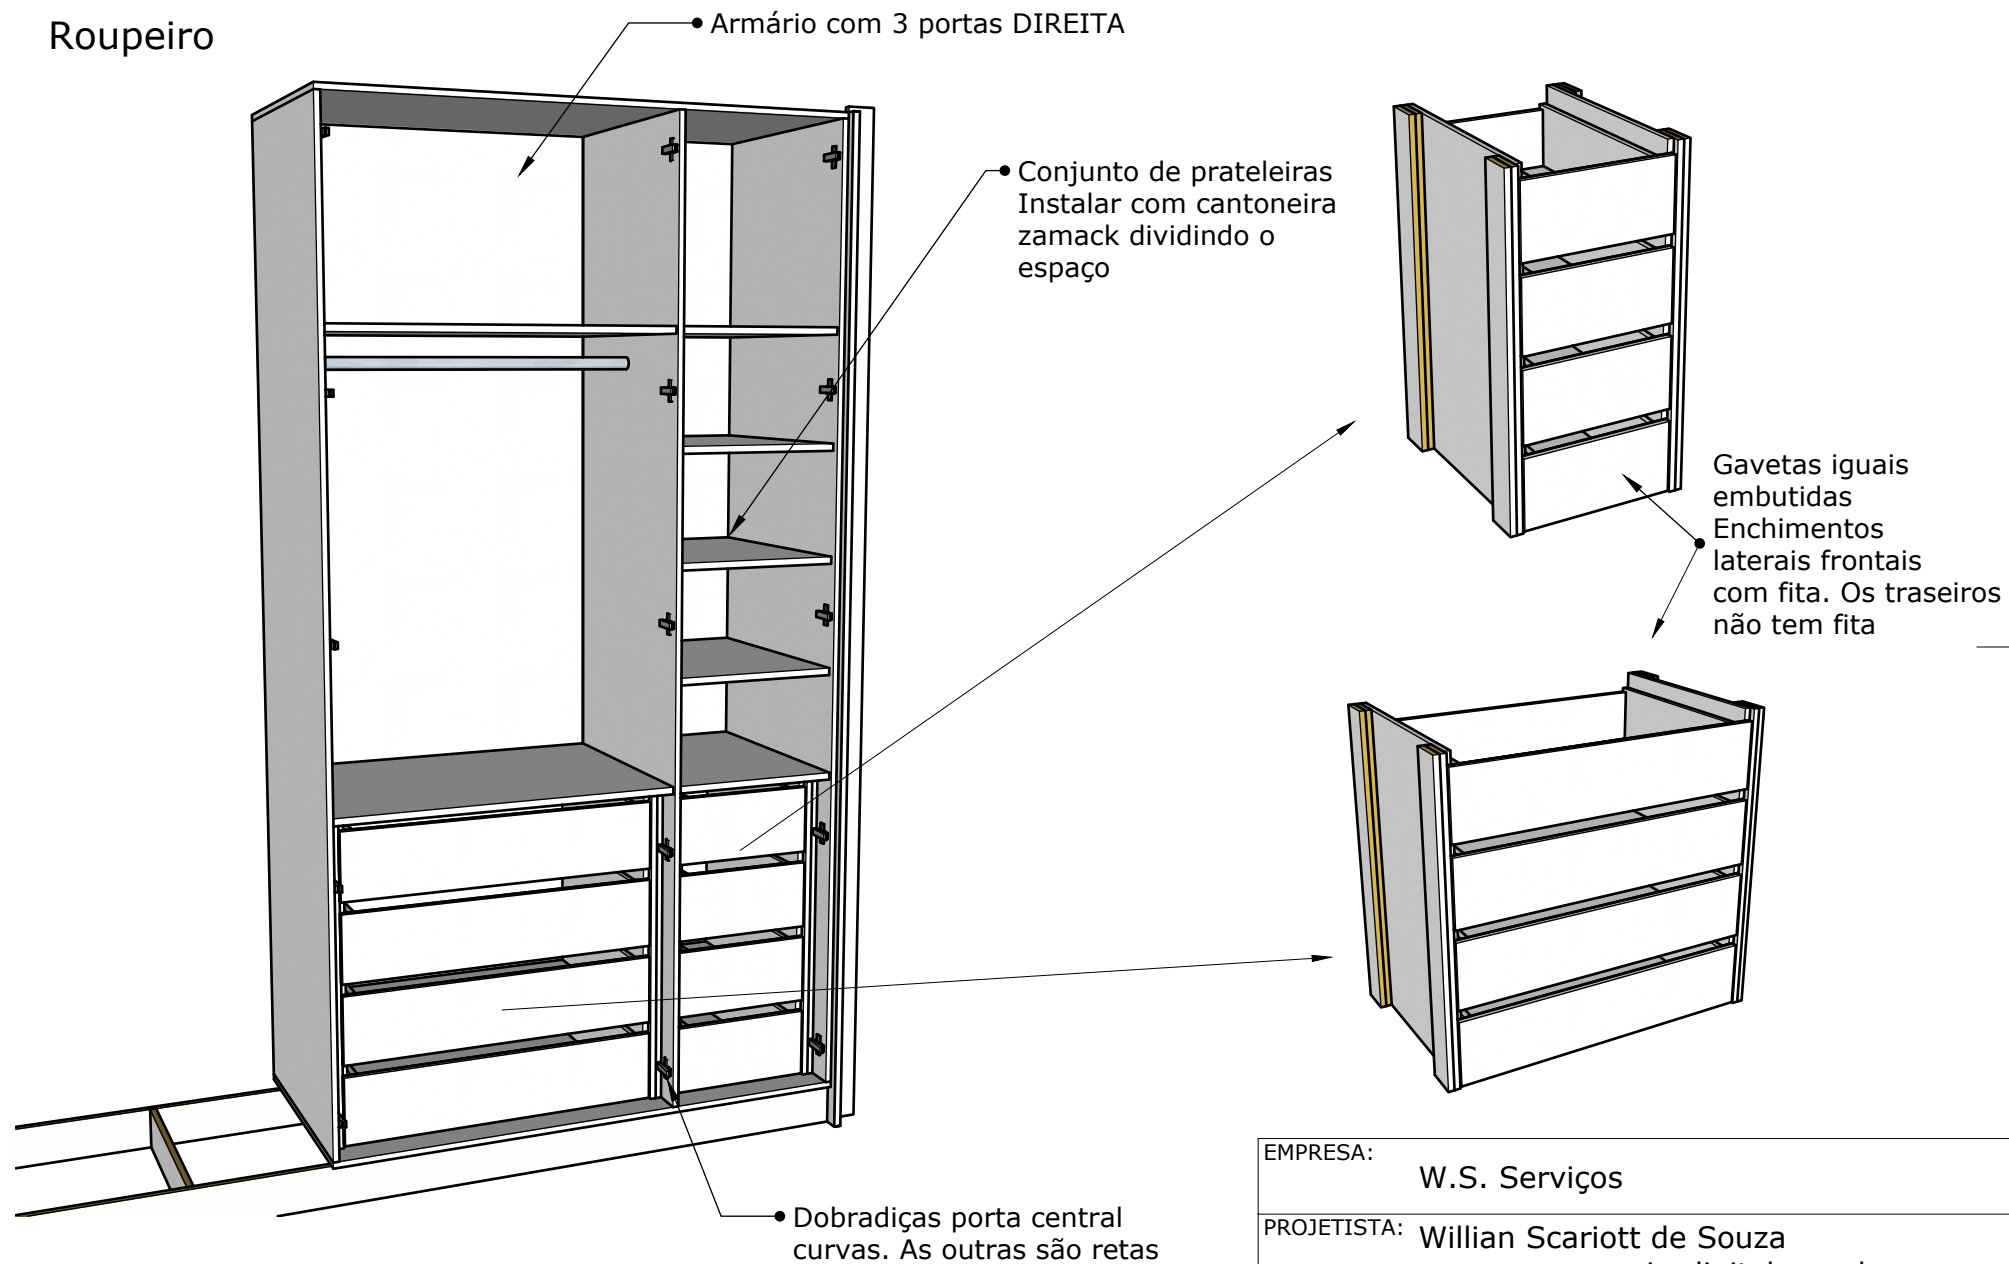

EMPRESA:

W.S. Serviços

PROJETISTA:

Willian Scariott de Souza

www.omarceneirodigital.com.br


CLIENTE:

Rodrigo e Bruna

Página: 9

Banheiro

Montagem do
corpo dos balcões
com minifix e
cavilha

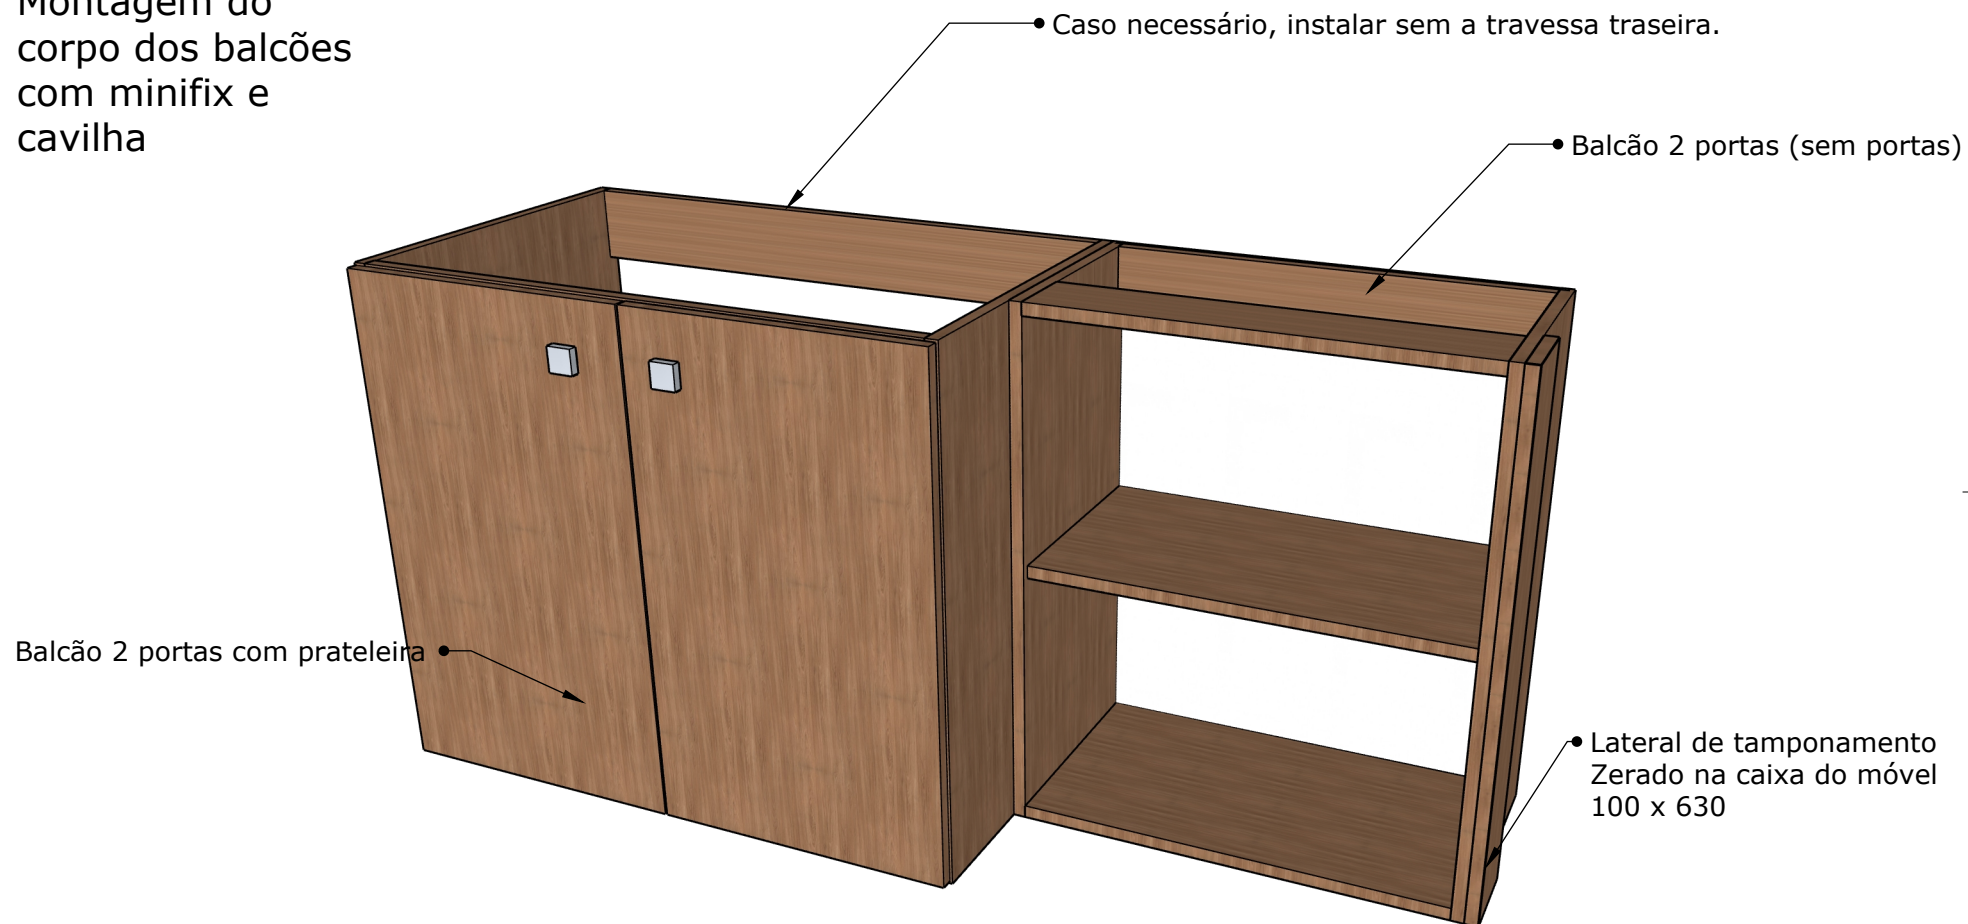

EMPRESA:	W.S. Serviços
PROJETISTA:	Willian Scariott de Souza www.omarceneirodigital.com.br
CLIENTE:	Rodrigo e Bruna

Banheiro



EMPRESA:	W.S. Serviços
PROJETISTA:	Willian Scariott de Souza www.omarceneirodigital.com.br
CLIENTE:	Rodrigo e Bruna

Escritório


Prateleiras instaladas com suporte invisível

Maiores na largura para ajuste na parede.

Confirmar com cliente a altura de cada. Se tem alturas diferentes ou todos espaços entre prateleiras são iguais. •

Rodapé recuado 23mm da frente da base (incluir painel amadeirado) •

03 balcões de 2 portas iguais
Todos dobradiças retas •

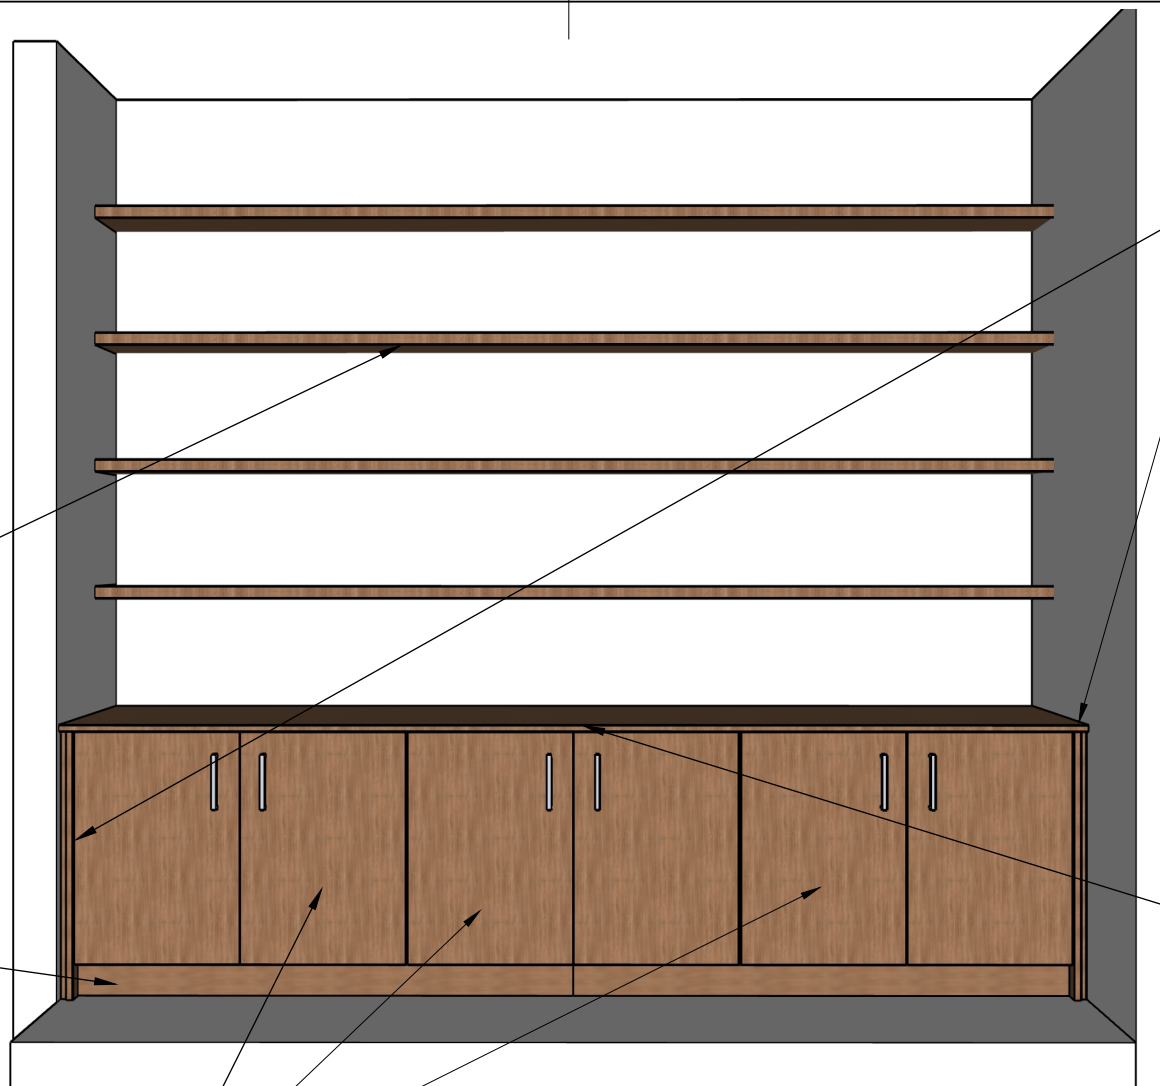

• Lateral de tamponamento avançando 22mm. 120 x 630

• Fixar tampo com parafusos por baixo
Cuidar para não passar para o tampo o parafuso

EMPRESA:

W.S. Serviços

PROJETISTA:

Willian Scariott de Souza

www.omarceneirodigital.com.br

CLIENTE:


Rodrigo e Bruna

Página: 1

Escritório

Rodapé em MDF branco, pode ser montado com parafusos.

Nivelar antes de colocar os balcões em cima •

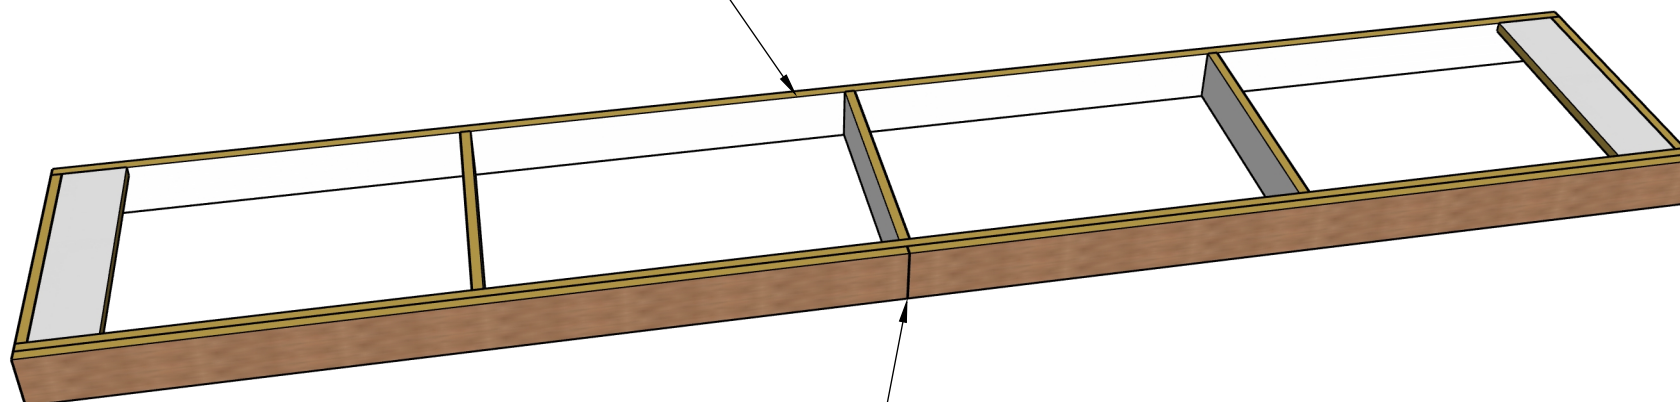

Painel Avulso
Frente do rodapé em
Carvalho. Colar com
cola instantânea •

EMPRESA:

W.S. Serviços

PROJETISTA:

Willian Scariott de Souza


www.omarceneirodigital.com.br

CLIENTE:

Rodrigo e Bruna


Página: 1

Escritório

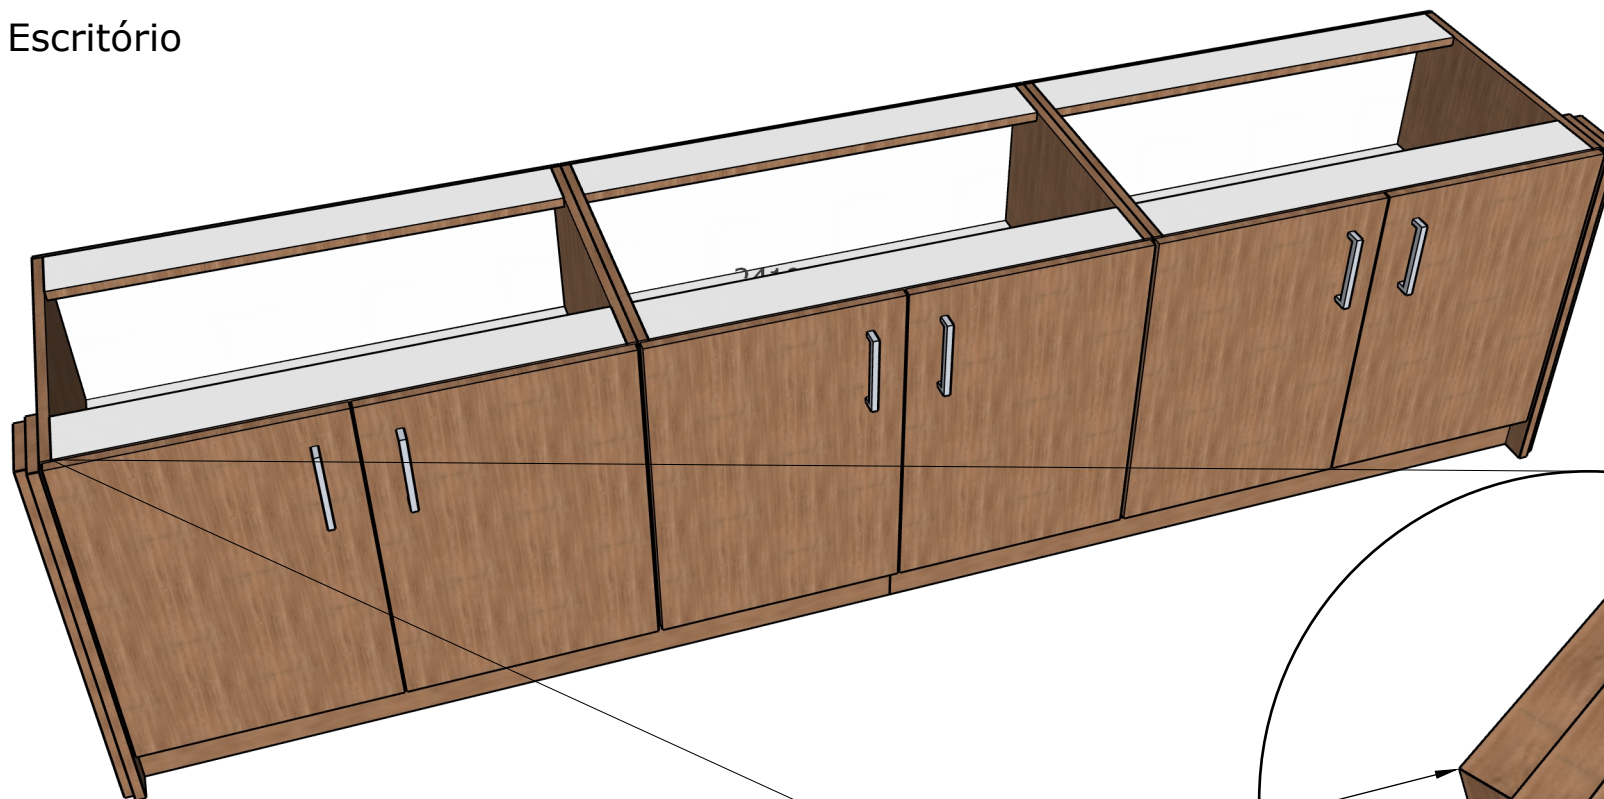

Lateral de tamponamento
recuado 10mm
100 x 630 •

Lateral de tamponamento avançando 22mm
120 x 630 •

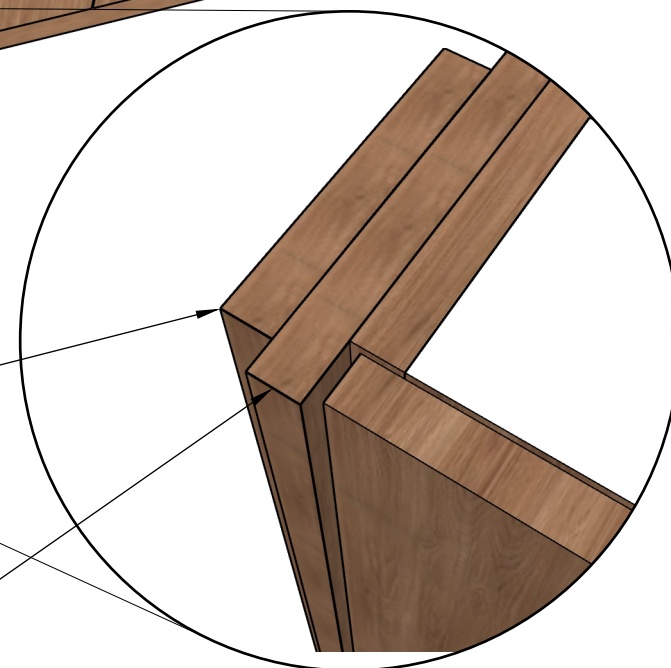

EMPRESA:

W.S. Serviços

PROJETISTA:

Willian Scariott de Souza

www.omarceneirodigital.com.br

CLIENTE:

Rodrigo e Bruna

Página: 1